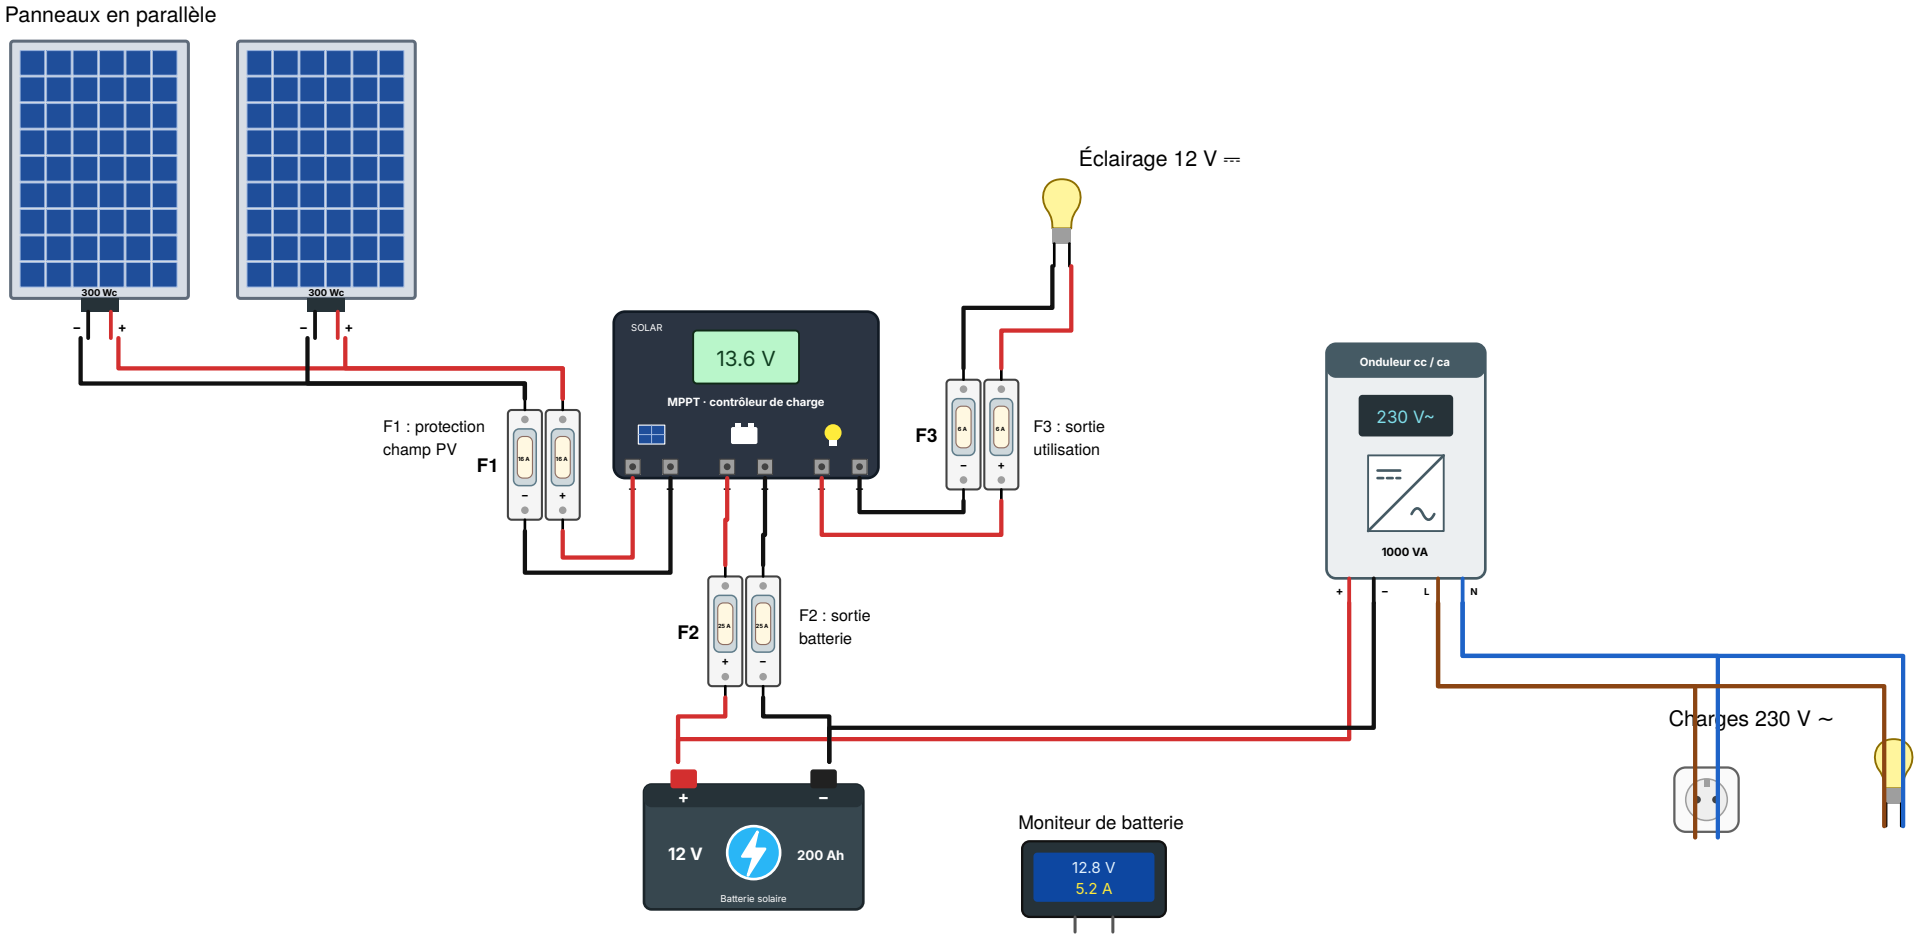Installation photovoltaïque en site isolé (12 V) — schéma technologique